


મોજે - ધનોલી
તાલુકો- ઉમરગામ
જિલ્લા- વલસાડ



૨૦૧૭-૧૮

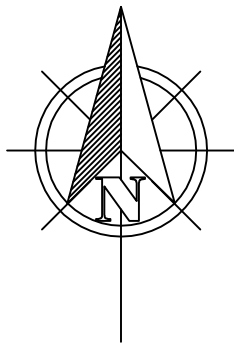

DHANOLI
UMARGAM
VALSAD
2017-18

સ્કેલ : ૧ મી. = ૨૦૦ મીટર
1: 2000

પ્રોજેક્ટન લીસ્ટન- વૃત્તીકલ્પ દુનવર્સ મંદિર - ૪૩ નોંધ
લોડીએન્ડન ડેમ- ડી ૧૫૫૭, ૧૫૫૮, ૧૫૫૯

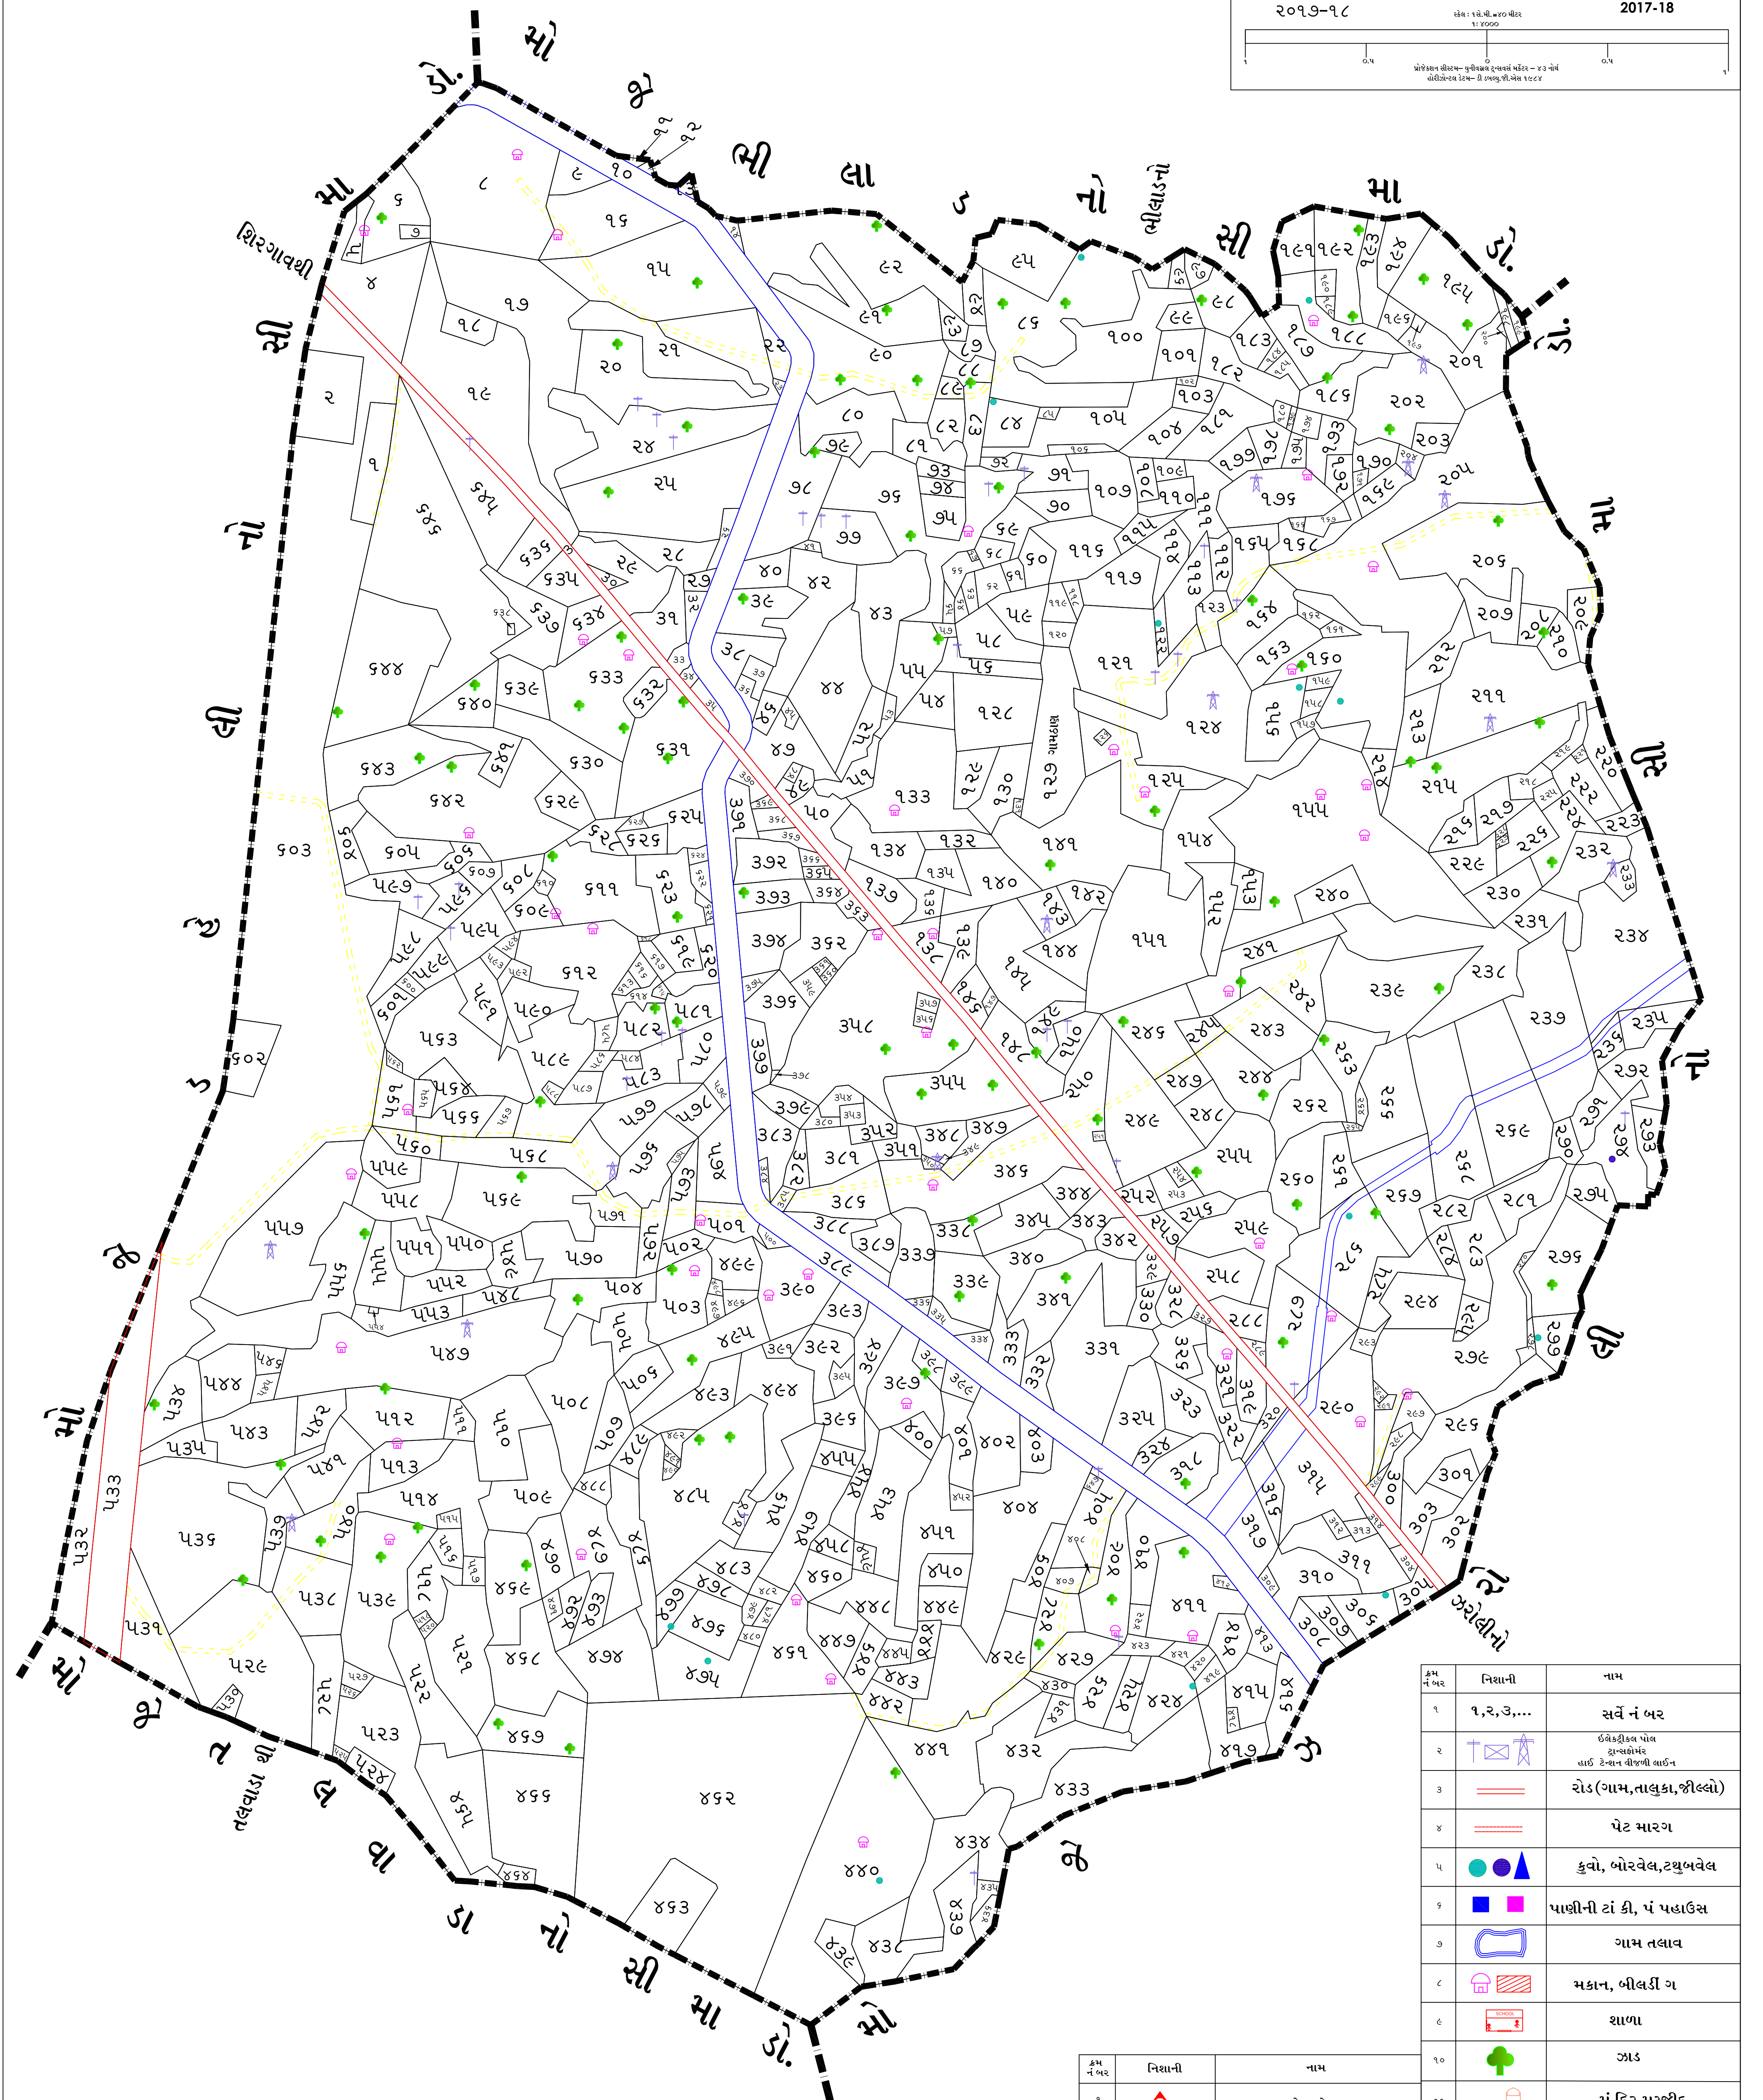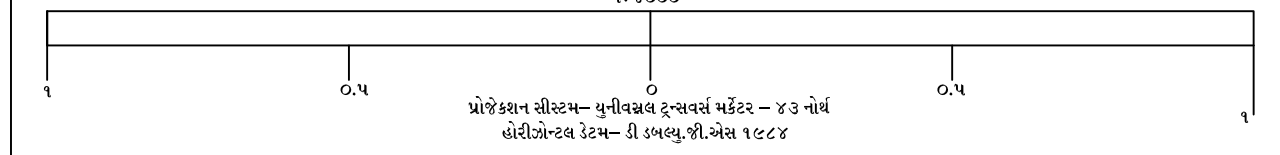

ક્રમ નં બર	નિશાની	નામ
૧	૧,૨,૩,...	સર્વે નં બર
૨	† ⊠ ⊡	ઇલેક્ટ્રીકલ પોલ ટ્રાન્સમિટર લાઈટ ટેન્શન લીજની લાઈન
૩	===	રોડ (ગામ, તાલુકા, જીલ્લો)
૪	===	પેટ મારગ
૫	● ● ▲	કુવો, બોરવેલ, ટચુબવેલ
૬	■ ■	પાણીની ટાં કી, પં પહાઉસ
૭	⬭	ગામ તલાવ
૮	⌂ ⬮	મકાન, બીલડી ગ
૯	⌂	શાળા
૧૦	♣	ઝાડ
૧૧	⌂	મં દિર મસ્જીદ
૧૨	—	કેનાલ
૧૩	~	નદીનાળા, કોતર
૧૪		રેલ્વે
૧૫	└┐	ગામ ની સીમડો

ક્રમ નં બર	નિશાની	નામ
૧	▲	બેસ સ્ટેશન
૨	○	રીજનલ સ્ટેશન
૩	◎	પ્રથમ કન્ટ્રોલ પોઈન્ટ
૪	★	દ્વિતીય કન્ટ્રોલ પોઈન્ટ
૫	▲	તૃતીય કન્ટ્રોલ પોઈન્ટ