




મોજે-એ કલેરે
તાલુકો-ઉમરગામ
જિલ્લા-વલસાડ
૨૦૧૭-૧૮

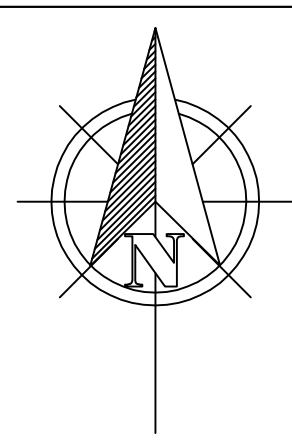

EKLAHARE
UMARGAM
VALSAD
2017-18

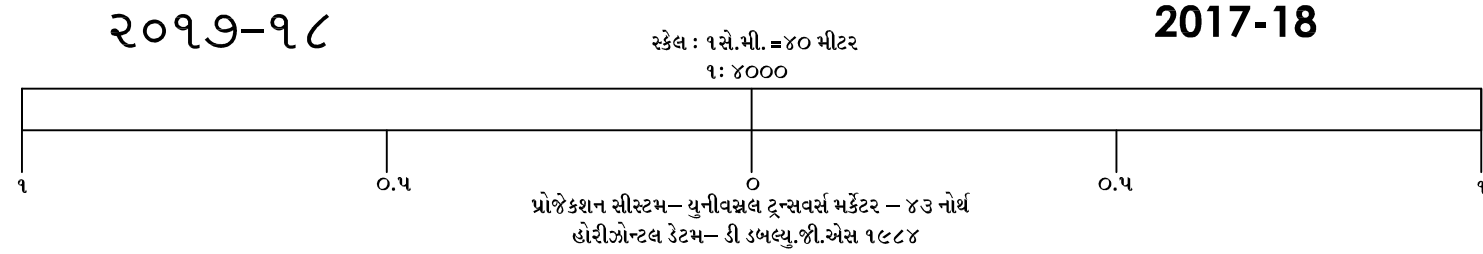

પ્રોજેક્ટન સીસ્ટમ- ગુનીવર્ત્તક રૂત્તવર્ત્ત મર્કેટર - ૪૩ નોર્થ
હોરીઝોન્ટલ ડેટમ- ડી ૩૫૯૫.૭૬ એલ ૧૯૮૮

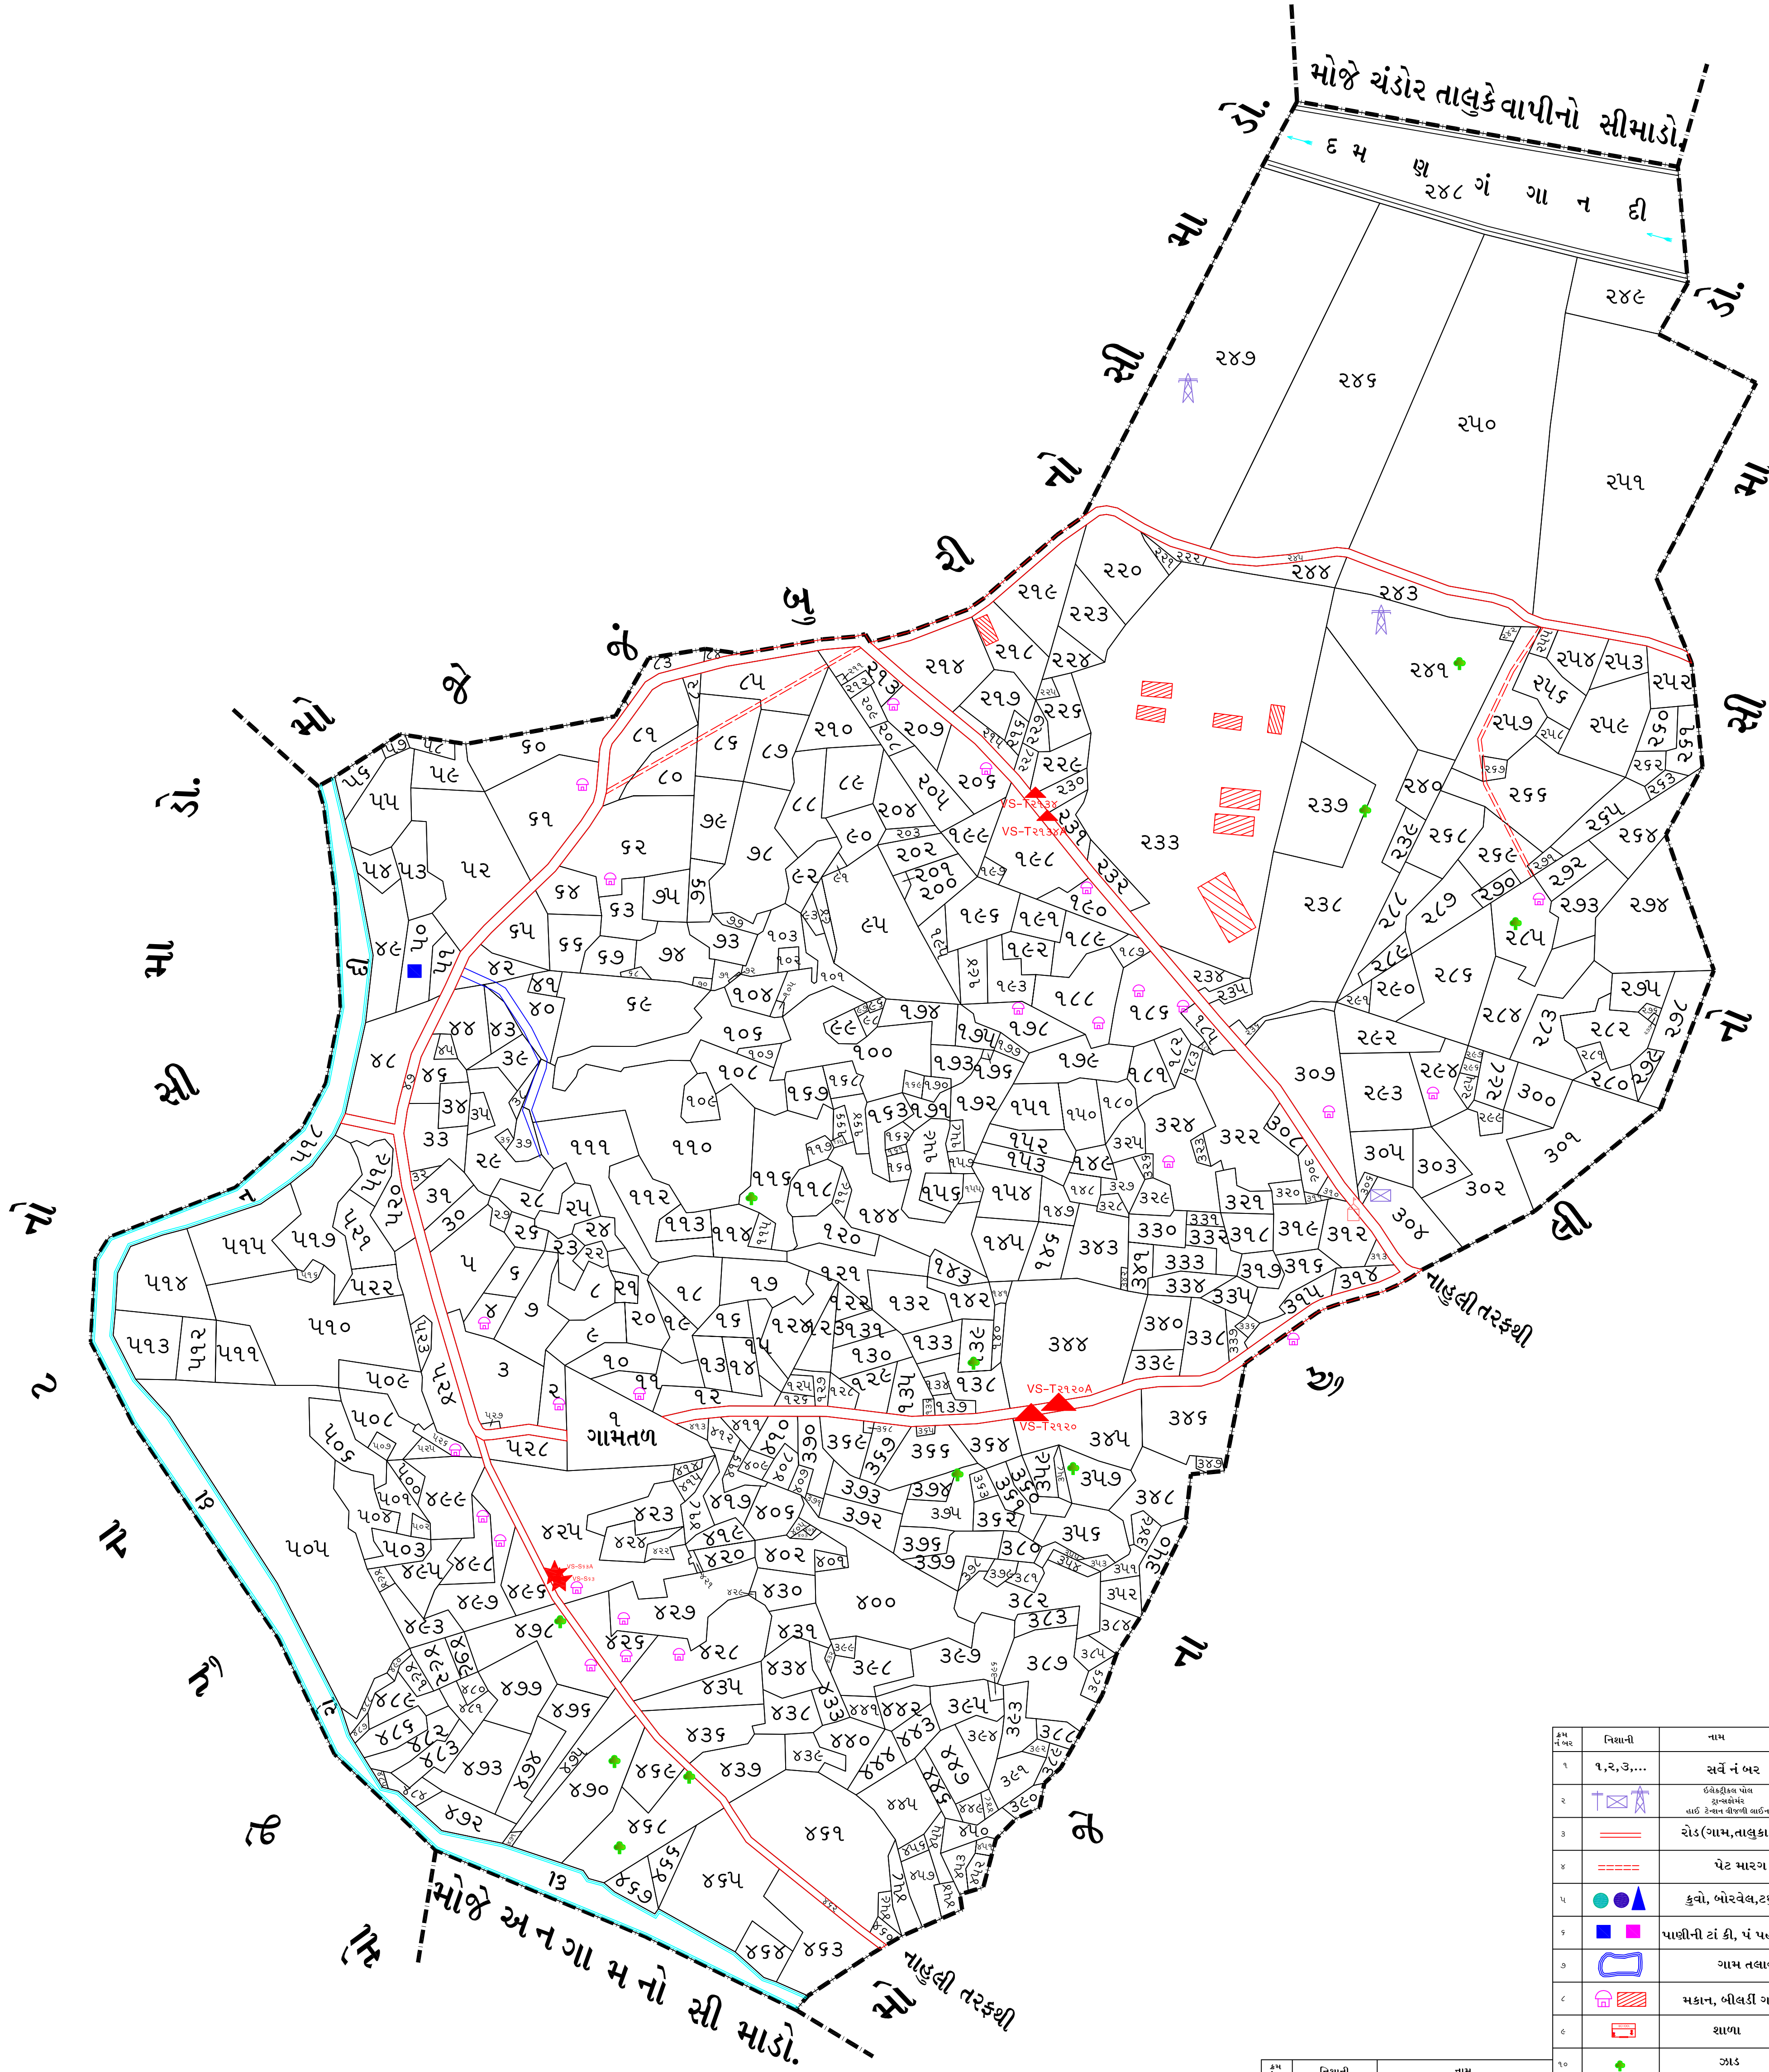

ક્રમ નંબર	નિશાની	નામ
૧	૧, ૨, ૩, ...	સર્વે નંબર
૨		ઉત્ક્રિષ્ટ પોલ ગુપ્તકોષ ભરૂં ટેન્શન લીનની વાઈન
૩		રોડ (ગામ, તાલુકા, જિલ્લો)
૪		પેટ મારગ
૫		કુવો, બોરવેલ, ટ્યુબવેલ
૬		પાણીની ટાંકી, પં પહાડેસ
૭		ગામ તલાવ
૮		મકાન, બીલડી ગ
૯		શાળા
૧૦		ઝાડ
૧૧		મંદિર મસ્જીદ
૧૨		કેનાલ
૧૩		નદીનાળા, કોતર
૧૪		રેલ્વે
૧૫		તુલીય કન્ઝોલ પોઈન્ટ

ક્રમ નંબર	નિશાની	નામ
૧		બેસ સ્ટેશન
૨		રીજનલ સ્ટેશન
૩		પ્રથમ કન્ઝોલ પોઈન્ટ
૪		દ્વિતીય કન્ઝોલ પોઈન્ટ
૫		તુલીય કન્ઝોલ પોઈન્ટ