




મોજે - નગવાસ
તાલુકો- ઉમરગામ
જિલ્લા- વલસાડ
2016-17

NAGWAS
UMARGAM
VALSAD
2016-17

સેક : 18, બ્લો : 100 મીટર
1:20000

પ્રોજેક્ટન લીટામ- સુલેશન ટુલ્સ વર્ક સેટ - 23 નેબ
સોલિડવર્ક 12મ- ડી ટ્રાન્સફોર્મ 10.0.4

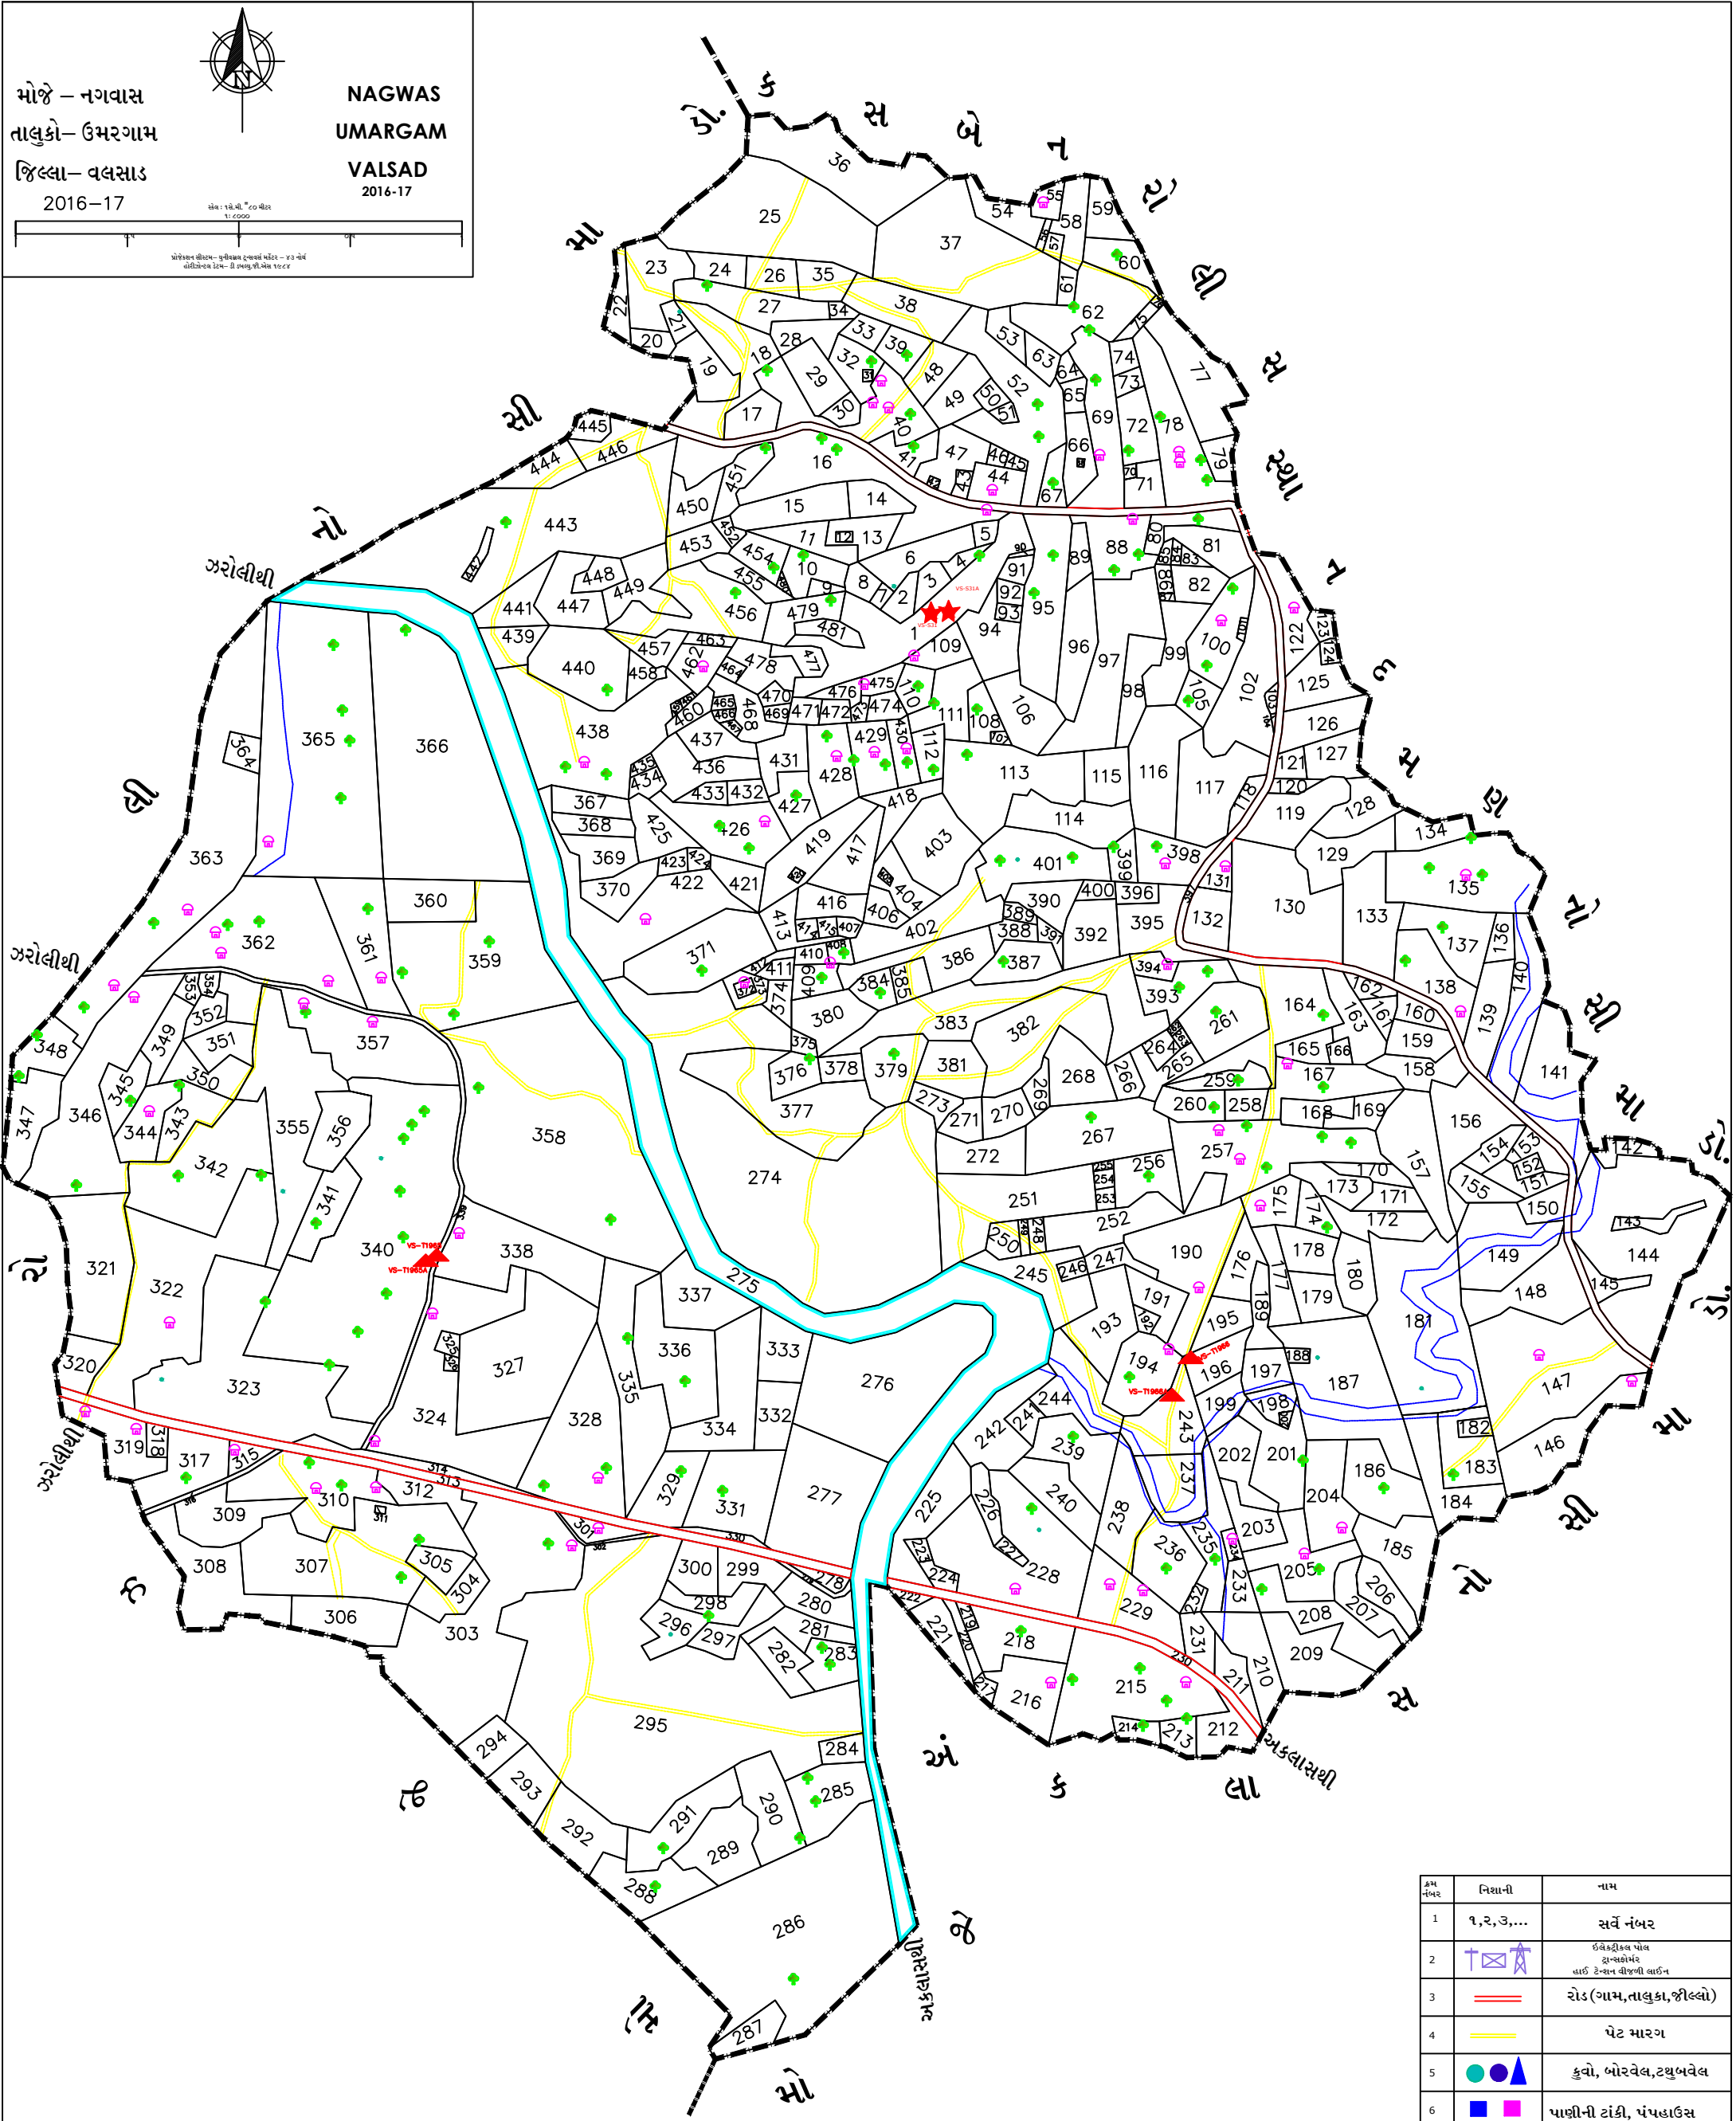

ક્રમ નંબર	નિશાની	નામ
1	૧,૨,૩,...	સર્વે નંબર
2		ઇલેક્ટ્રીકલ પોલ ગ્રાન્ડેસ્ટેશન લાઈટ ટેન્શન લીટામી લાઈન
3		રોડ (ગામ, તાલુકા, જિલ્લો)
4		પેટ મારગ
5		કુવો, બોરવેલ, ટ્યુબવેલ
6		પાણીની ટાંકી, પંપહાઉસ
7		ગામ તલાવ
8		મકાન, બીલડીંગ
9		શાળા
10		ઝાડ
11		મંદિર મસ્જીદ
12		કેનાલ
13		નદીનાળા, કોતર
14		રેલ્વે
15		ગામ ની સીમડો

ક્રમ નંબર	નિશાની	નામ
1		બેસ સ્ટેશન
2		રીજનલ સ્ટેશન
3		પ્રથમ કન્ડ્રોલ પોઈન્ટ
4		દ્વિતીય કન્ડ્રોલ પોઈન્ટ
5		તૃતીય કન્ડ્રોલ પોઈન્ટ