


મોજે – નારગોલ
તાલુકો- ઉંમરગામ
જિલ્લા- વલસાડ

૨૦૧૭-૧૮


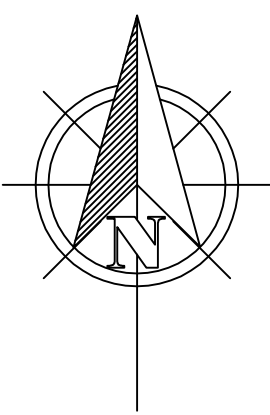


NARGOL
UMARGAON
VALSAD
2017-18

સ્કેલ : ૧ સે.મી. = ૮૦ મીટર

૧: ૮૦૦૦

પ્રોજેક્ટન ચોરસ- વૃત્તીચલ ટ્રસ્ટવર્ક મેપર- ૪૩ નંબર
પોલીટોપલ ડેપુટી- ડી.કે.એલ.જી.એસ ૧૯૮૪

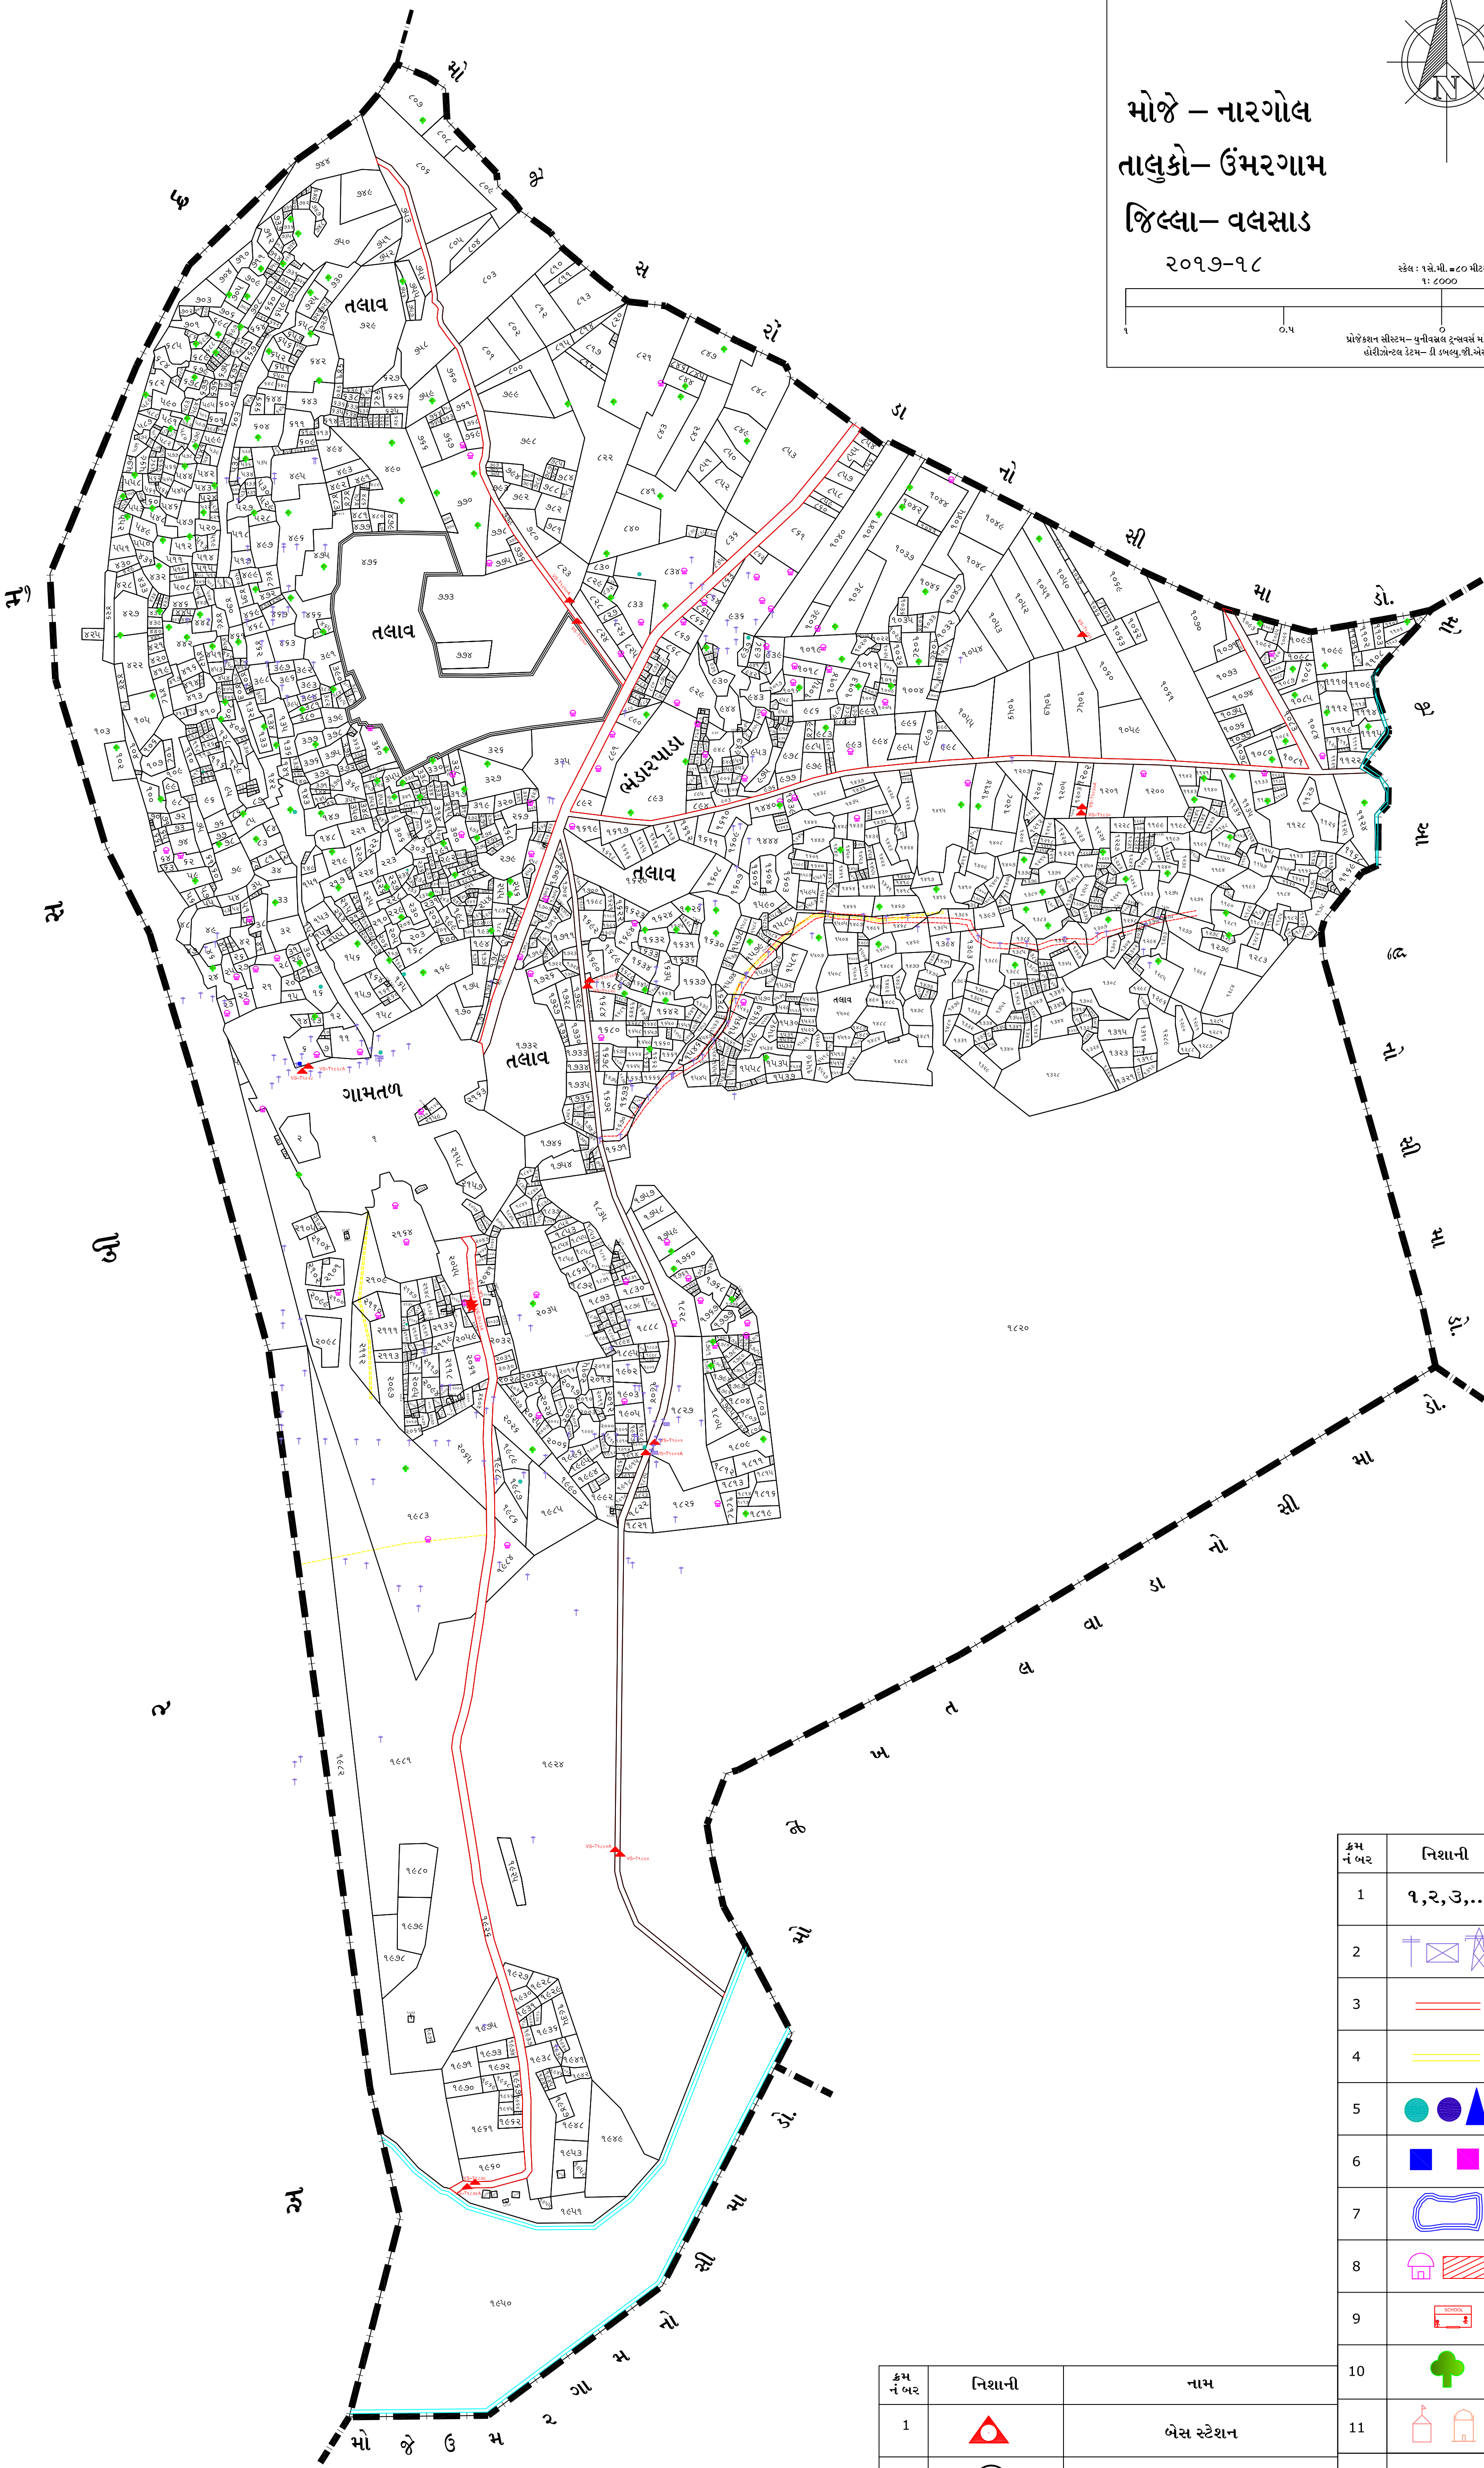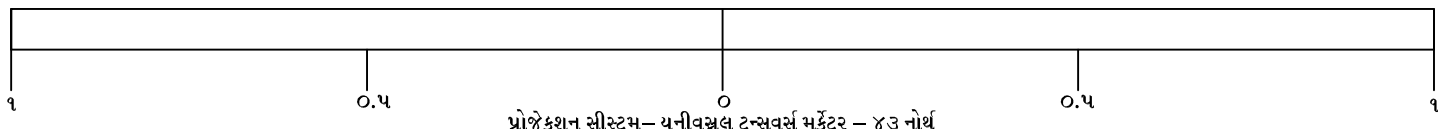

ક્રમ નંબર	નિશાની	નામ
1	૧, ૨, ૩, ...	સર્વે નંબર
2		ઇલેક્ટ્રીકલ પોલ ટ્રાન્સફોર્મર હાઈ ટેન્શન વીજળી લાઈન
3		રોડ (ગામ, તાલુકા, જિલ્લો)
4		પેટ મારગ
5		કુવો, બોરવેલ, ટથુબવેલ
6		પાણીની ટાંકી, પં પહાઉસ
7		ગામ તલાવ
8		મકાન, બીલડી ગ
9		શાળા
10		ઝાડ
11		મંદિર મસ્જીદ
12		કેનાલ
13		નદીનાળા, કોતર
14		રેલ્વે
15		ગામ ની સીમડો

ક્રમ નંબર	નિશાની	નામ
1		બેસ સ્ટેશન
2		રીજનલ સ્ટેશન
3		પ્રથમ કન્ટ્રોલ પોઈન્ટ
4		દ્વિતીય કન્ટ્રોલ પોઈન્ટ
5		તૃતીય કન્ટ્રોલ પોઈન્ટ